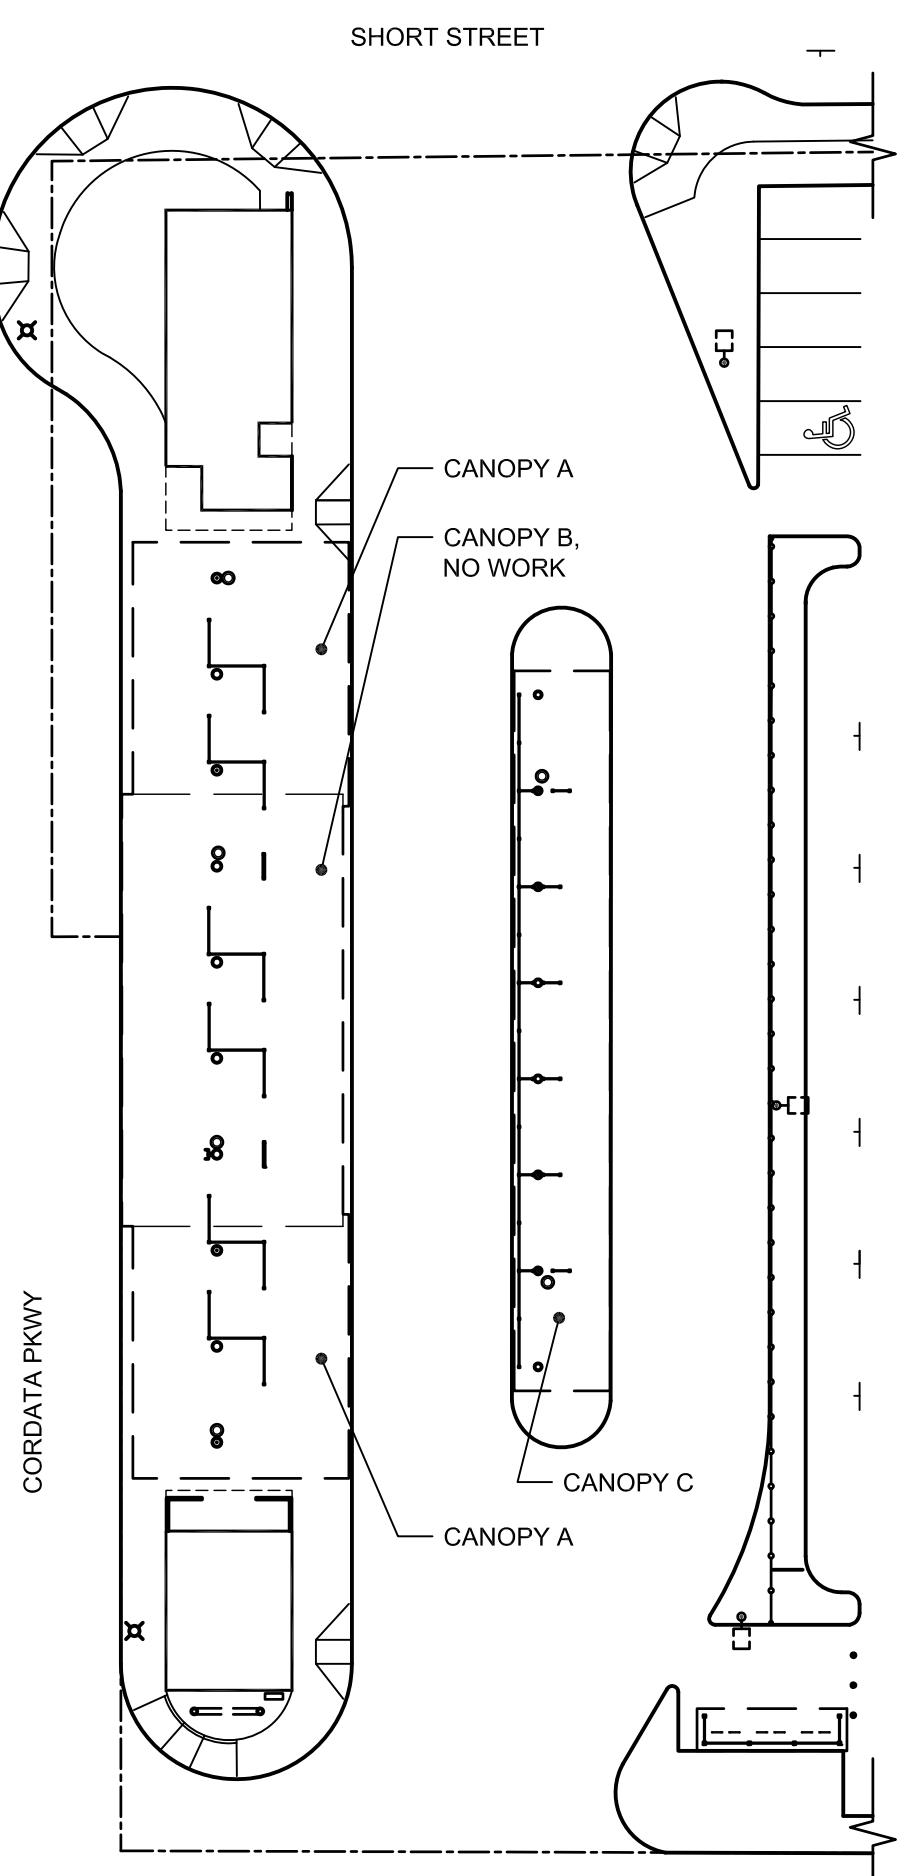


ARCHITECTURAL ABBREVIATIONS

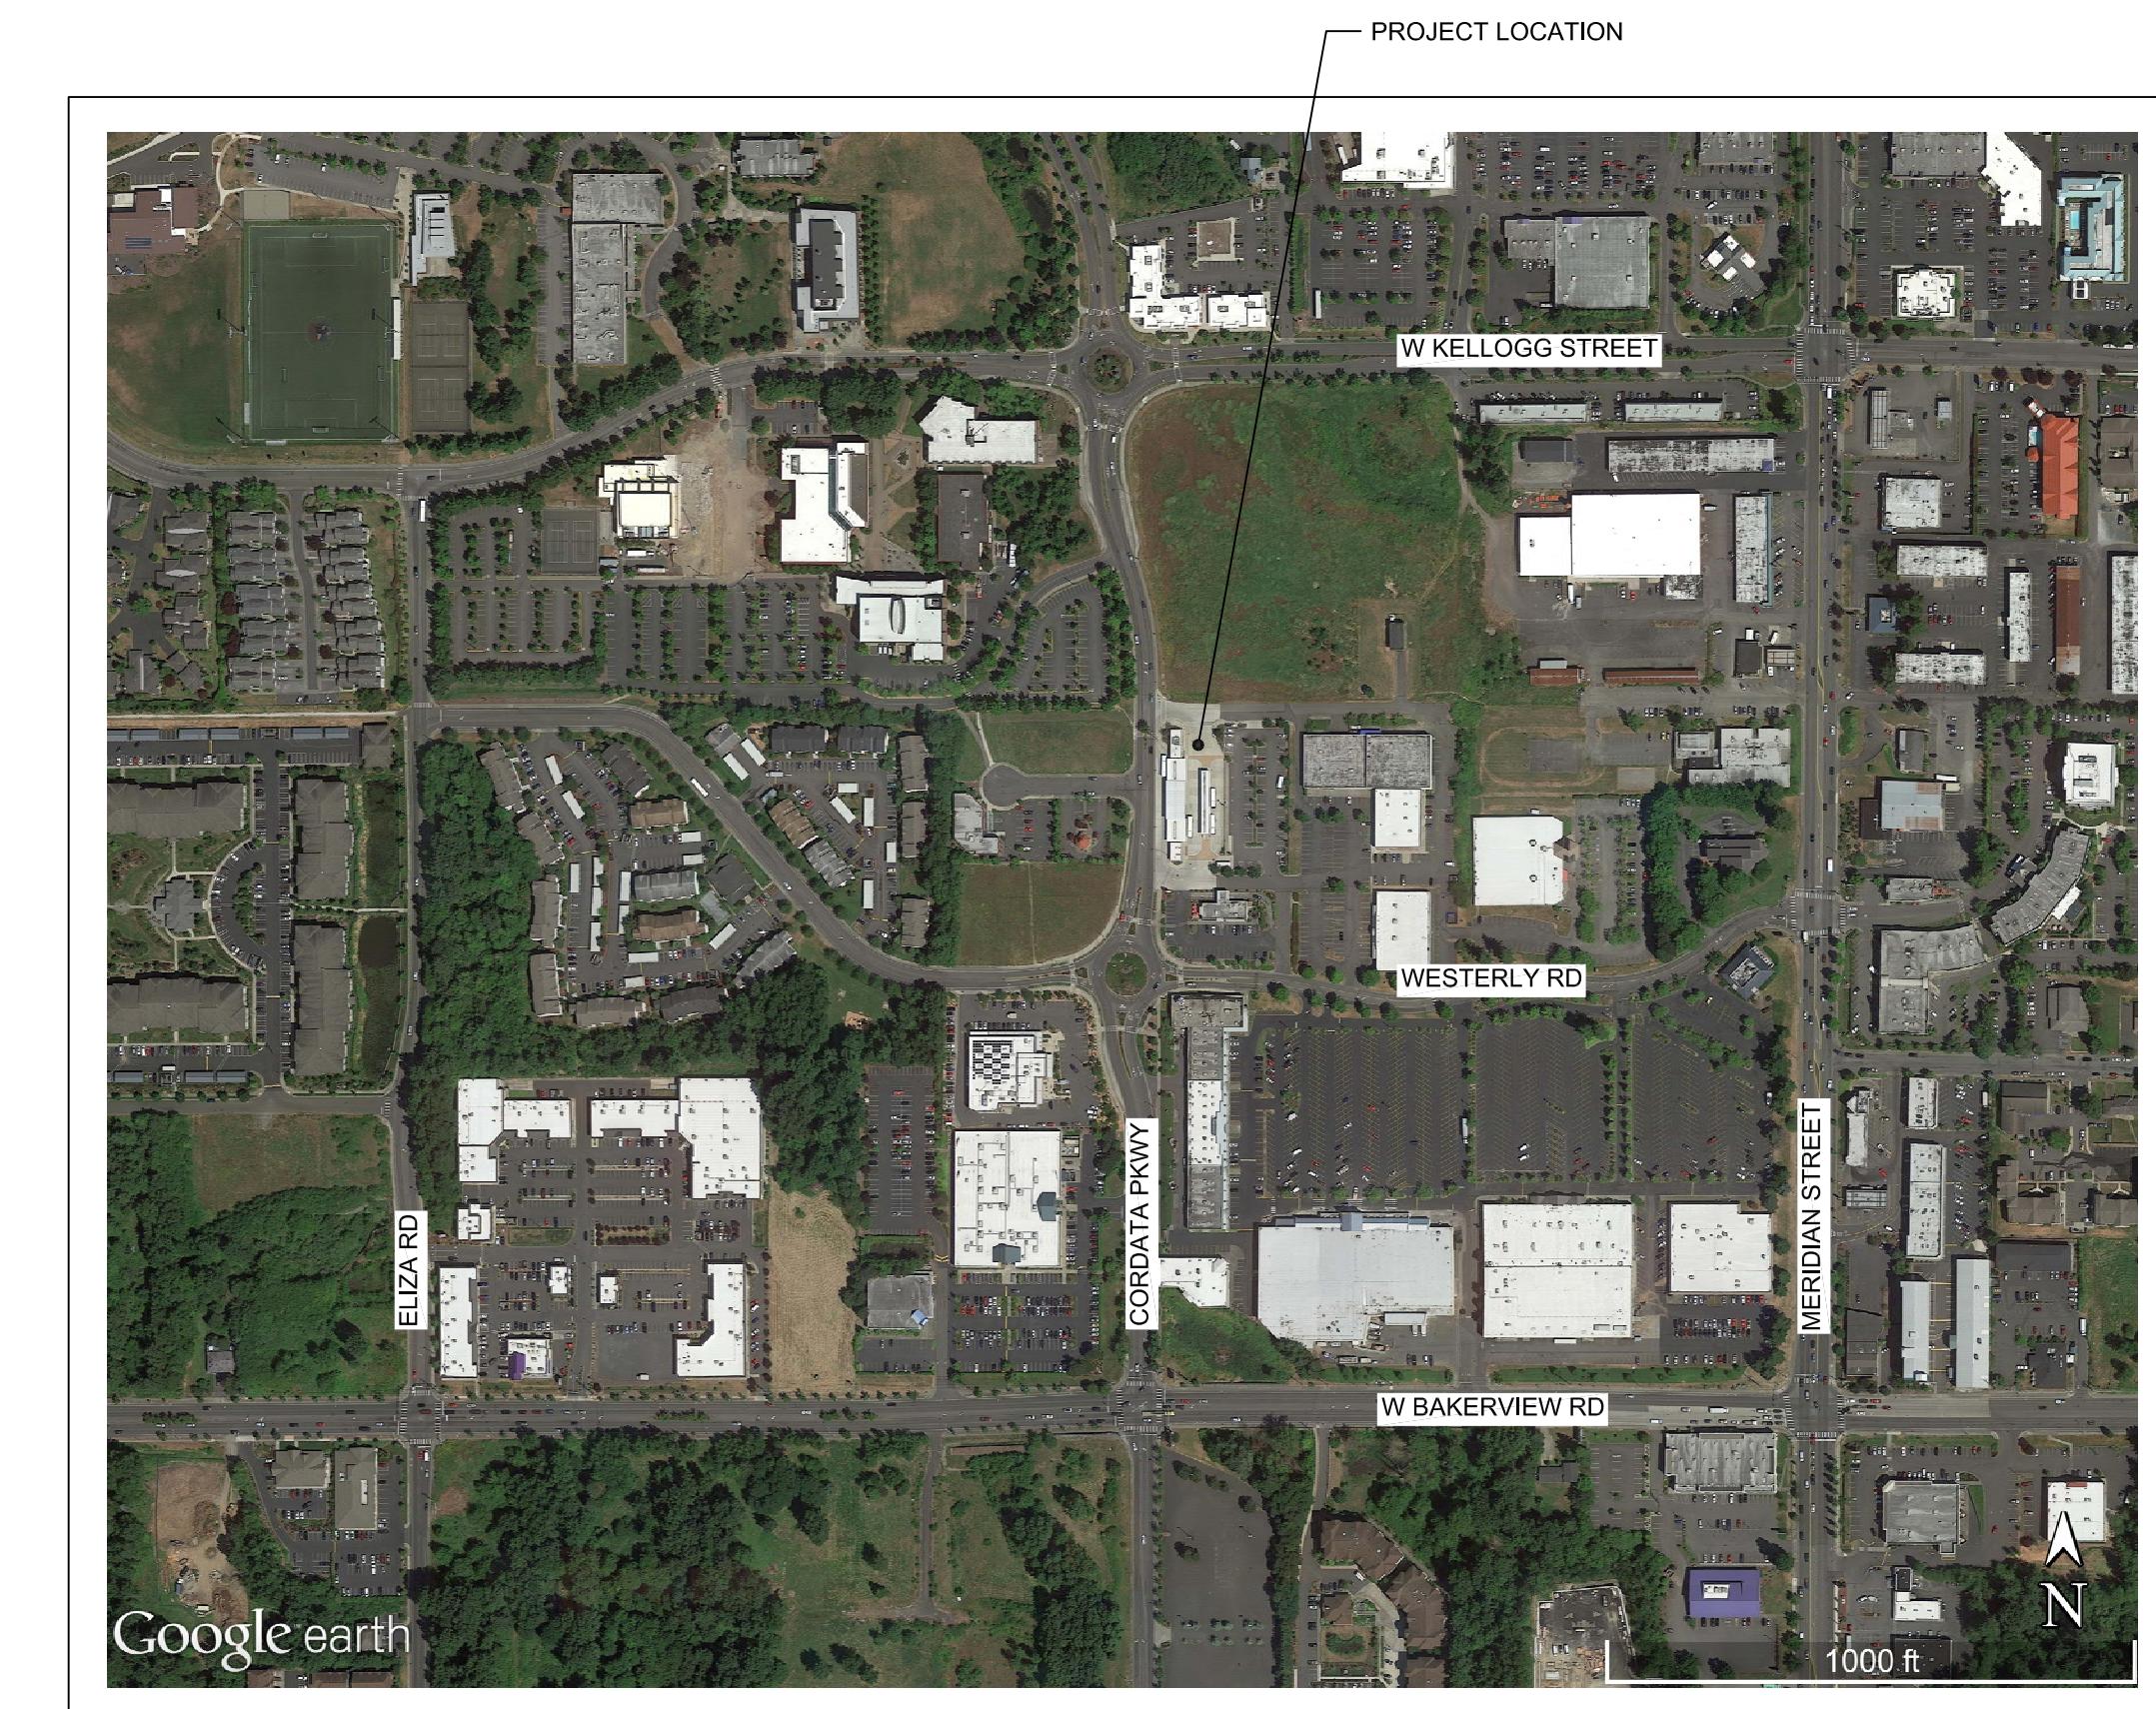
AFF	ABOVE FINISHED FLOOR
ALUM	ALUMINUM
AHU	AIR HANDLING UNIT
ALT	ALTERNATE
AV	AUDIO / VISUAL
BLDG	BUILDING
DIA	DIAMETER
DS	DOWNSPOUT
ELEC	ELECTRICAL
ELEV	ELEVATOR/ELEVATION
ENL	ENLARGED
EXIST	EXISTING
EXT	EXTERIOR
FCP	FIBER CEMENT PANEL
FE	FIRE EXTINGUISHER
FEC	FIRE EXTINGUISHER CABINET
FF	FINISH FLOOR
FRT	FIRE RETARDANT TREATED
FF SAM	FOIL FACED SELF-ADHERED MEMBRANE
GA	GAUGE
GLB	GLUE LAMINATED BEAM
GWB	GYPSUM WALLBOARD
HR	HOUR
INSUL	INSULATION
HSS	HOLLOW STEEL SECTION
HT SAM	HIGH TEMP RESISTANT SELF-ADHERED MEMBRANE
LF	LINEAL FEET
INT	INTERIOR
MFR	MANUFACTURER
MECH	MECHANICAL
MISC	MISCELLANEOUS
NA	NOT APPLICABLE
NFVA	NET FREE VENT AREA
NIC	NOT IN CONTRACT
OC	ON CENTER
OPP	OPPOSITE
PT	PRESSURE TREATED
REF	REFERENCE/REFRIGERATOR
RM	ROOM
SF	SQUARE FOOT
SI	SQUARE INCH
SHT	SHEET
SIM	SIMILAR
SQU	SQUARE
SS	STAINLESS STEEL
ST	STREET
STRUCT	STRUCTURAL
TOC	TOP OF CONCRETE
TYP	TYPICAL
UNO	UNLESS NOTED OTHERWISE
WC	WATER CLOSET
WD	WOOD
W/	WITH
@	AT
&	AND



PARTIAL SITE PLAN

SCALE: 1/32" = 1'-0"

SITE INFO

4194 CORDATA PKWY
BELLINGHAM, WA 98226

PROJECT LOCATION

VICINITY MAP

N.T.S.

OWNER

WHATCOM TRANSPORTATION AUTHORITY
4111 BAKERVIEW SPUR
BELLINGHAM, WA 98226

DRAWING INDEX

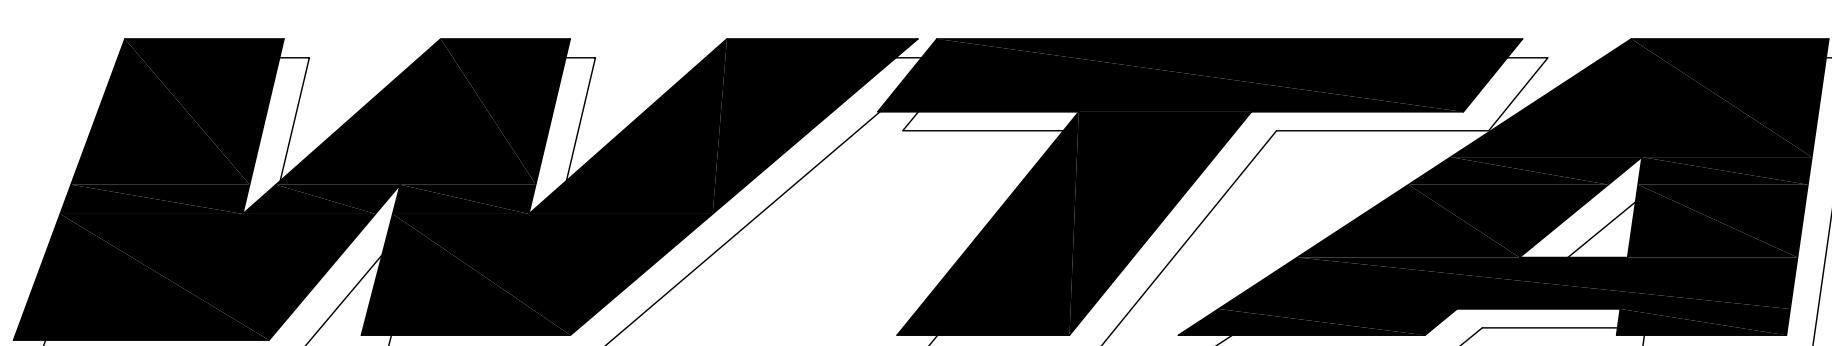
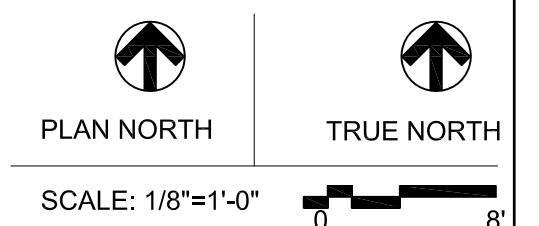
GENERAL	
G1.01	: PROJECT & SITE INFORMATION
ARCHITECTURAL	
A3.01	: ELEVATIONS

DESIGN TEAM

ARCHITECTS
ZERVAS
209 PROSPECT STREET
BELLINGHAM, WA 98225
360.734.4744

BID SET

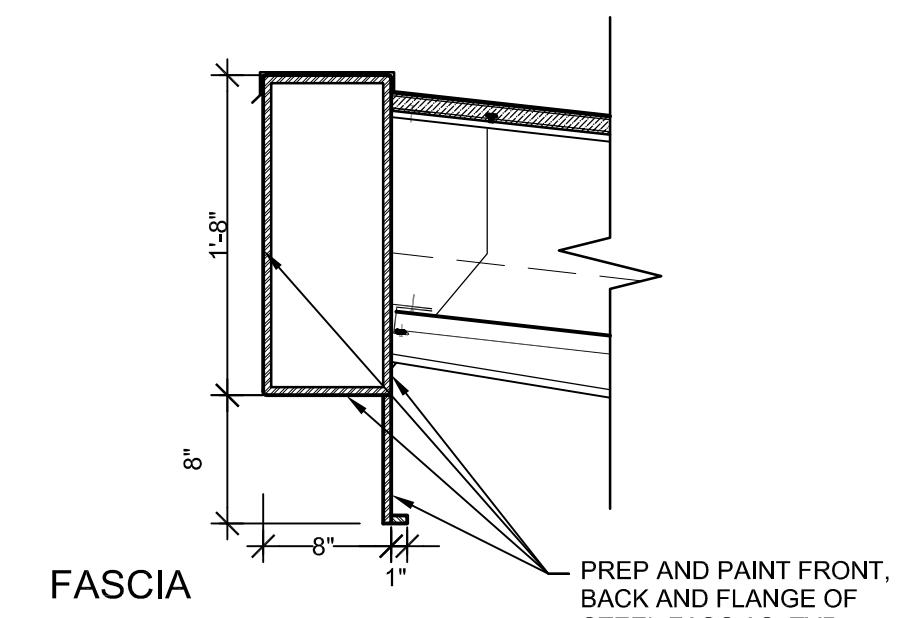
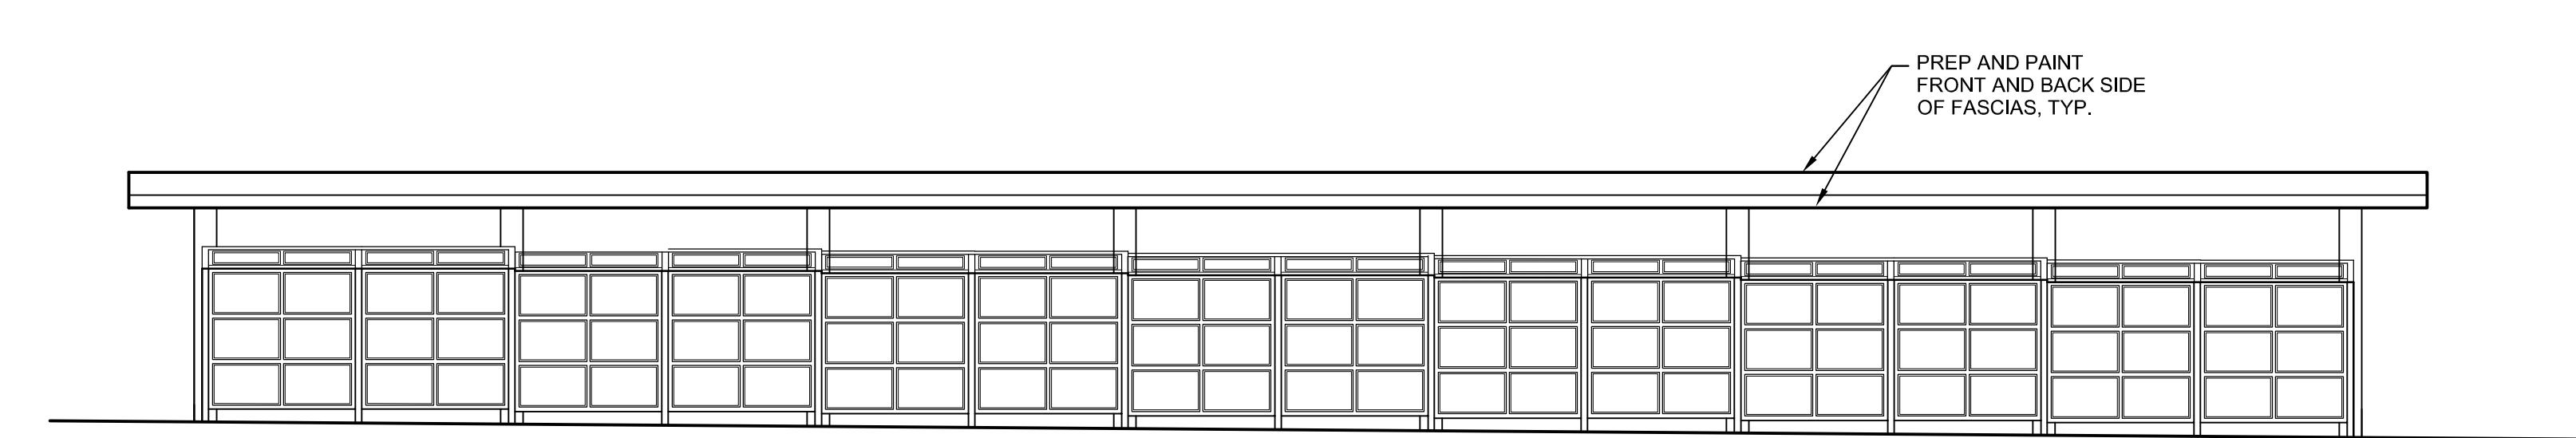
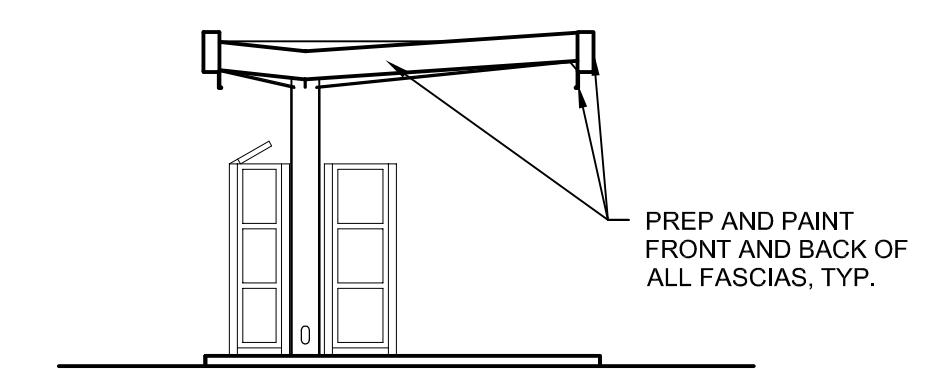
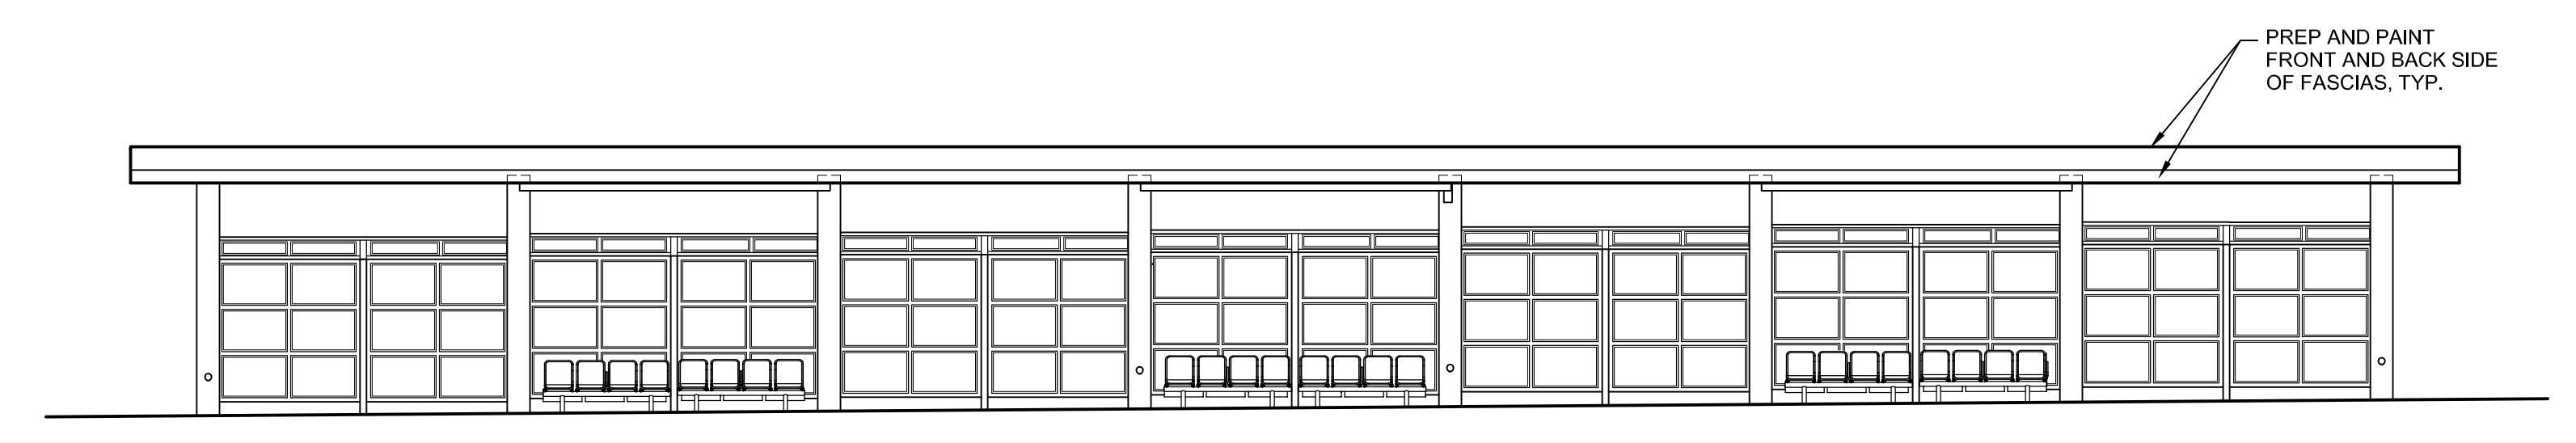
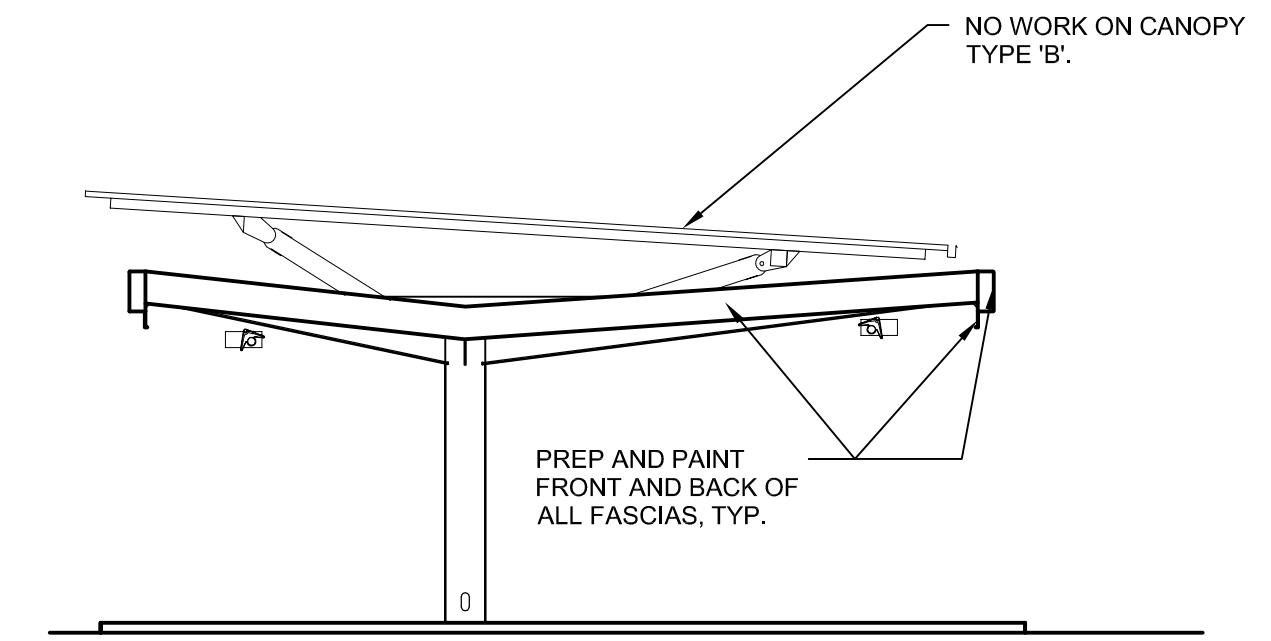
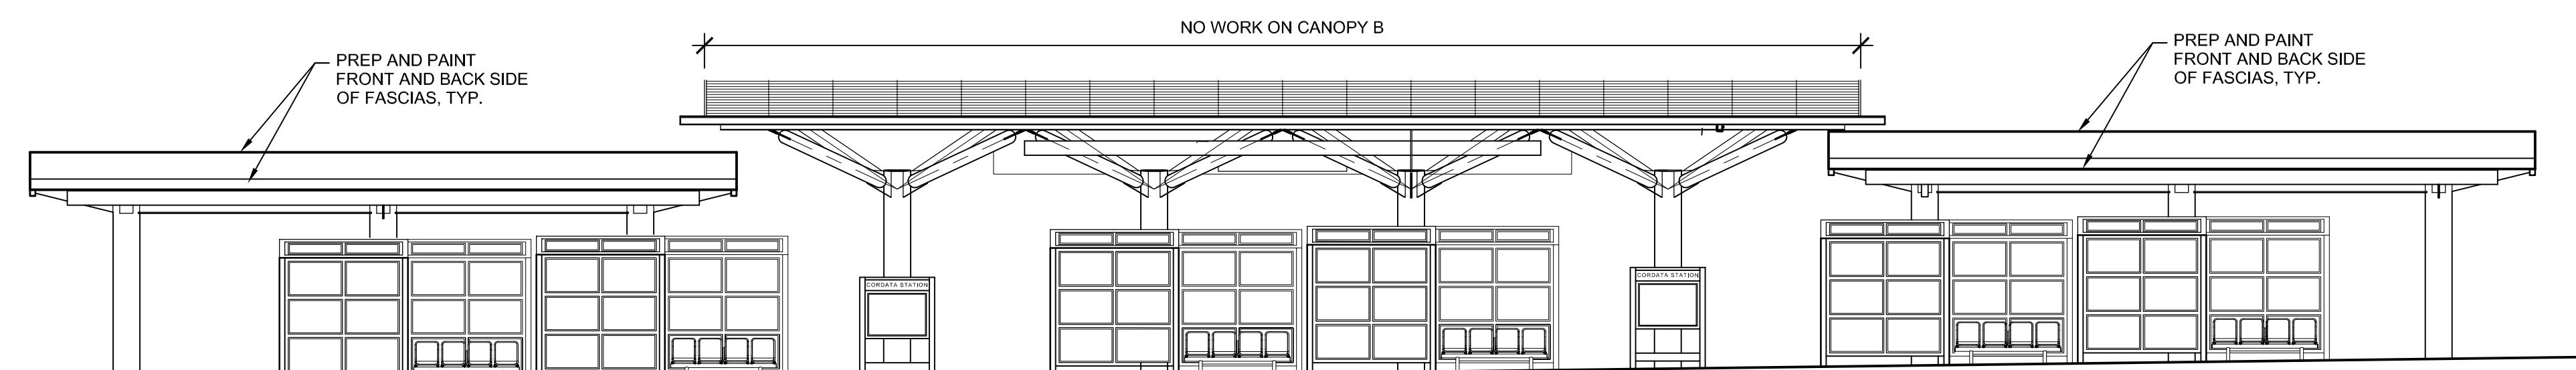
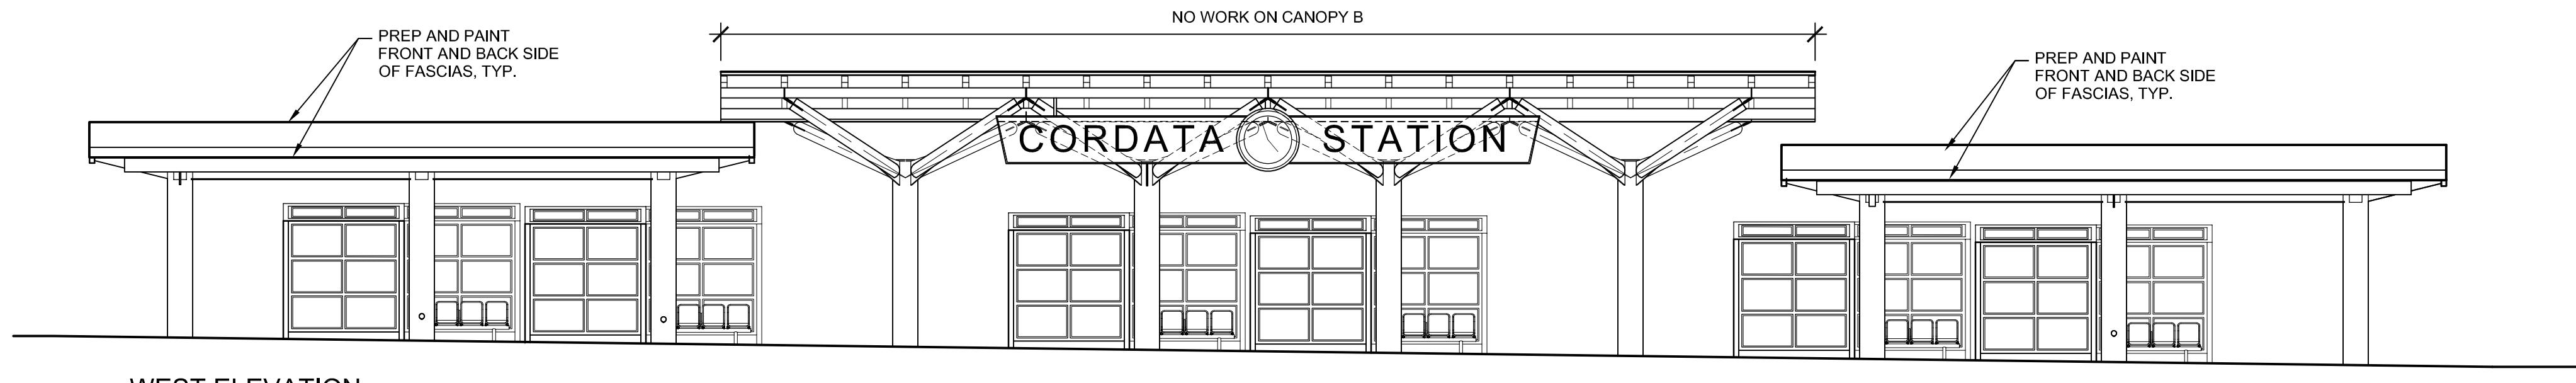
REV	ISSUED FOR	DATE



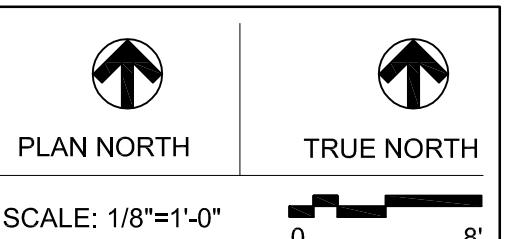
Whatcom Transit Authority

Cordata Station Repaint

WTA CORDATA STATION REPAINT ALTERNATE #2	
WHATCOM TRANSIT AUTHORITY	
PROJECT & SITE INFO	
PROJECT No:	201502.05
DRAWN BY:	SJAB
CHECKED BY:	XX
DATE ISSUED:	07.15.2015
G1.01	
© 2014	

**BID SET**

REV	ISSUED FOR	DATE

**WTA CORDATA STATION REPAINT ALTERNATE #2****WHATCOM TRANSIT AUTHORITY ELEVATIONS**

PROJECT No: 201502.05
DRAWN BY: SJAB
CHECKED BY: XX
DATE ISSUED: 07.15.2015

A3.01